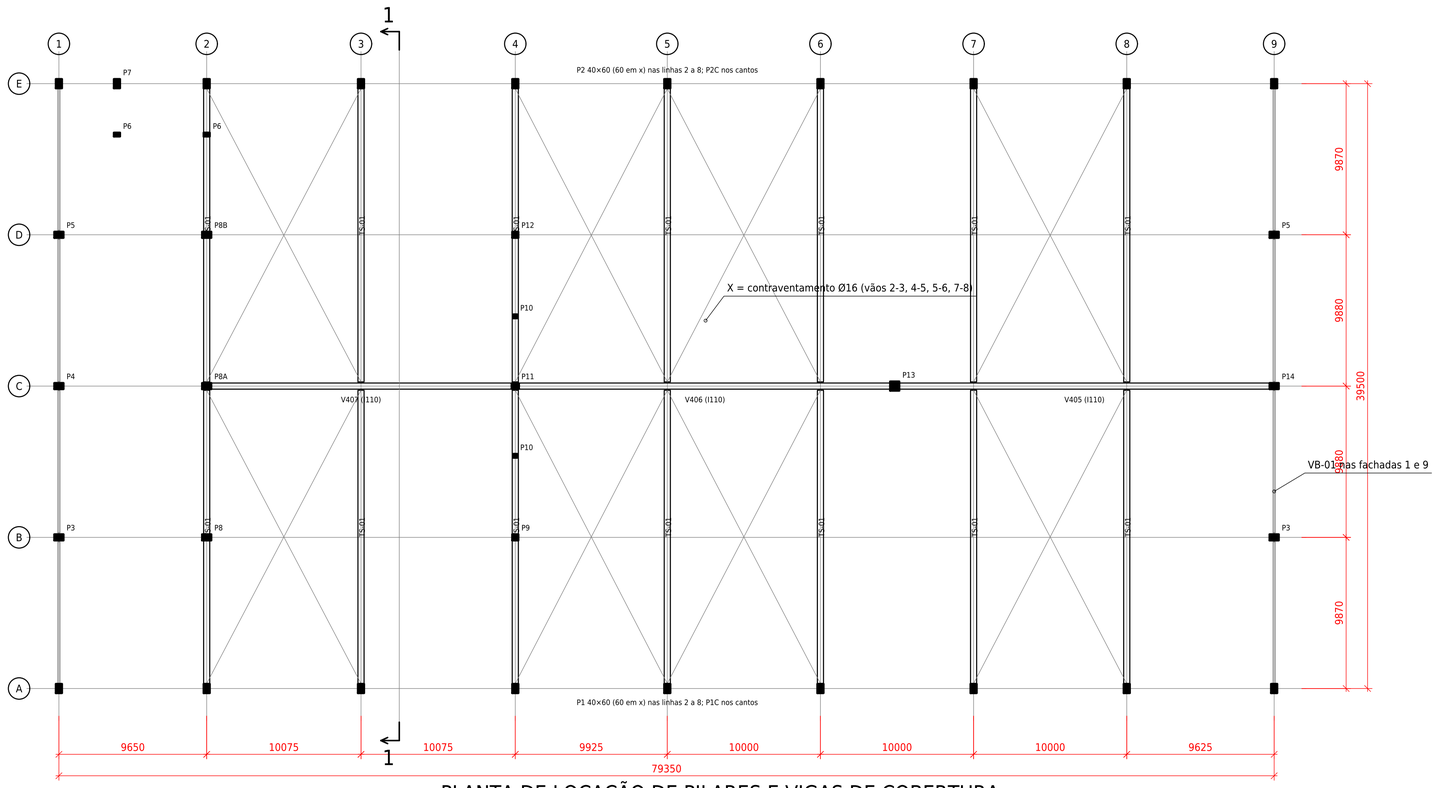


PLANTA DE LOCAÇÃO DE PILARES E VIGAS DE COBERTURA

ESC. 1:200 — COTAS EM MM — eixos e ordenadas do R01; contraventamento da cobertura em X

PILARES (R01)


MARCA	SEÇÃO	QT	POSIÇÃO	CABEÇA
P1 / P2	40×60	14	laterais (A e E), linhas 2–8	recuo +8,40 (A) / +9,55 (E)
P1C / P2C	40×60	4	cantos	recuo nas duas faces internas
P3 P4 P5 / P3 P14 P5	40×60	6	fachadas 1 e 9	recuo acima da VB
P8 P8B / P8A	40×60	3	linha 2 (mezanino / eixo C)	-
P9 P11 P12 / P10	40×40 / 25×25	5	linha 4 (portões)	-
P13	60×60	1	eixo C (apoio V405/V406)	-
P6 / P7	25×40 / 60×40	3	anexo do eixo E	-

VIGAS DE COBERTURA

MARCA	SEÇÃO	QT	L (m)	POSIÇÃO
TS-01	I90	14	19,15	cobertura, linhas 2 a 8 (2 por linha)
V407	I110	1	19,60	eixo C, linha 2 → linha 4
V406	I110	1	24,23	eixo C, linha 4 → P13
V405	I110	1	24,23	eixo C, P13 → linha 9
VB-01	15×70	8	≈ 9,3	bordas das fachadas 1 e 9


NOTAS

1. Geometria do R01 (locação de pilares): 79,35 m entre os eixos 1 e 9; 39,50 m entre os eixos A e E. Água única de 3 %, subindo de A para E; cobertura escondida pela platibanda +10,00 (placas por fora dos pilares).
2. RECUO DOS PILARES (a validar): acima do topo da TS-01 junto à face do pilar (+8,40 no eixo A, +9,55 no eixo E) o pilar sobe só com os 300 mm externos (cabeça 40×30) até +10,00, segurando as placas da platibanda. A telha e a calha (lado A) correm retas por dentro da linha das cabeças; o contra-rufo é reto, fixado nas placas entre pilares e na face da cabeça nos pilares (retorno de 30 cm só), sem rufos grandes contornando o pilar. No lado E (alto) a telha fica 12 cm abaixo do topo e o rufo-capa cobre placa + faixa do recuo.
3. TS-01 apoiada nos consolos CP-TS dos pilares (eixos A e E) e nos consolos CV-TS da I110 ou dos pilares P8A/P11 (eixo C), com dente 45×30, neoprene e pino PN-1 Ø20.
4. Contraventamento da cobertura em X Ø16 nos vãos 2-3, 4-5, 5-6 e 7-8 (ND-LET-COB02).
5. Níveis em metros a partir do piso acabado; cotas em mm. Conferir a locação com o arquitetônico.
6. PROJETO DA ND ENGENHARIA — PARA APROVAÇÃO, NÃO EXECUTAR.

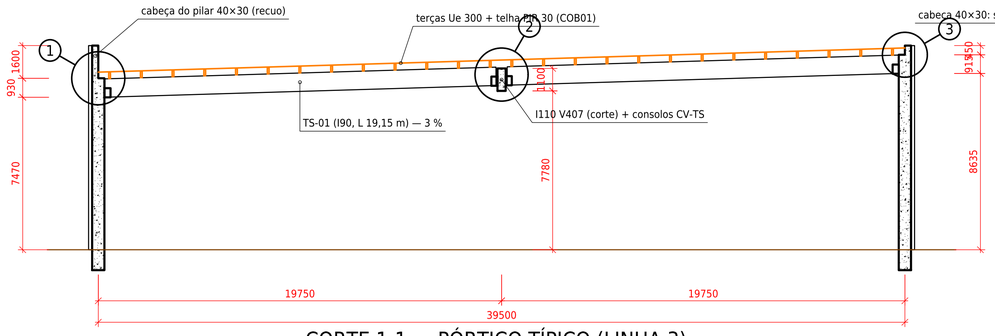


CORTE 1-1 — PÓRTICO TÍPICO (LINHA 3)

ESC. 1:150 — COTAS EM MM — água única 3 % (sobe de A para E); TS-01 nos consolos dos pilares e da I110; cobertura escondida na platibanda +10,00

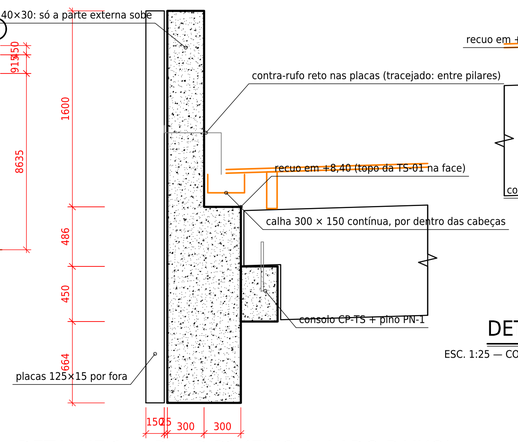


DETALHE 1 — PILAR P1 (EIXO A, LADO BAIXO)

ESC. 1:25 — COTAS EM MM — TS-01 no consolo CP-TS; cabeça do pilar recuada; placas por fora até +10,00

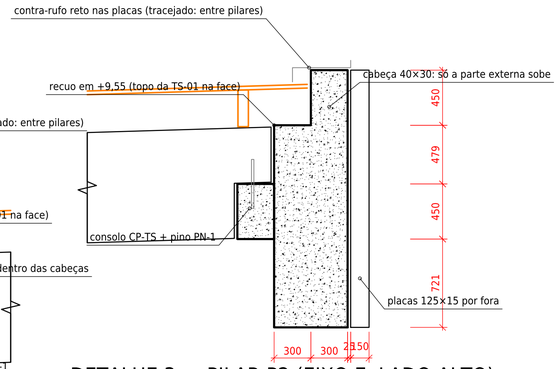

DETALHE 3 — PILAR P2 (EIXO E, LADO ALTO)

ESC. 1:25 — COTAS EM MM — TS-01 no consolo CP-TS; cabeça do pilar recuada; placas por fora até +10,00

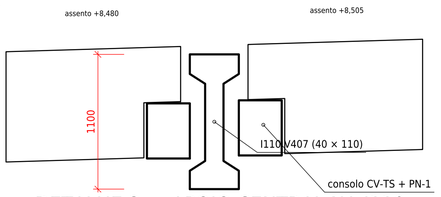

DETALHE 2 — APOIO CENTRAL NA I110

ESC. 1:25 — COTAS EM MM — duas TS-01 com dente nos consolos CV-TS

REV	DATA	DESCRIÇÃO
01	12/10/2026	geometria do R01 (79,35 × 39,50 m); corte 1-1 refeito; recuo dos pilar

ND ENGENHARIA E ASSESSORIA LTDA — PARA APROVAÇÃO

CNPJ 46.745.157/0001-47 · ndengenharia.com · WhatsApp (46) 92000-4685 · Saudade do Iguaçu/PR

RESP. TÉCNICO: Eng. Civil Nathan Henrique Delgado — CREA-SC 168298-1

ART Nº: _____

CLIENTE: MARQUES ENGENHARIA E CONSTRUÇÕES

OBRA: LETSARA — PAVILHÃO COM MEZANINO

LOCAL: A CONFIRMAR

CONTEÚDO: LOCAÇÃO DE PILARES E VIGAS DE COBERTURA — CORTE DO PÓRTICO E RECUO DOS PILARES NA PLATIBANDA

ESCALA	DATA	DESENHO	VERIFICADO	APROVADO
INDICADAS	12/10/2026	ND Engenharia	-	-

DESENHO Nº	REV.	FOLHA	FORMATO
ND-LET-LOC01	01	01/01	A1

1º DIEDRO