
eixos A e E, linhas 2 a 9; fundo +7,50, topo +8,10; dentes Gerber 30 × 20 nos consolos CP-VT (assento +7,79); atrás da fiada de placas +7,50/+8,75

VT — VIGA DE TRAVAMENTO 25 × 60 cm — L = 922,5 A 967,5 cm — 14 PEÇAS

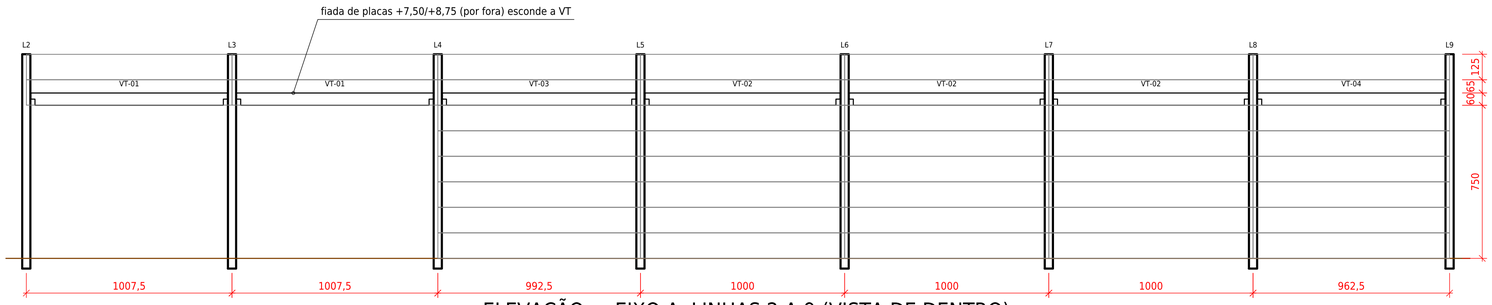

ELEVAÇÃO — EIXO A, LINHAS 2 A 9 (VISTA DE DENTRO)

ESC. 1:150 — COTAS EM CM — VT atrás das placas; linhas 2-4: placas só acima de +7,50

MARCAS — VT 25×60 (eixos A e E)

MARCA	TRECHO (linhas)	QT	L (cm)	PESO (t)
VT-01	L2–L3, L3–L4	4	967,5	3,70
VT-02	L5–L6, L6–L7, L7–L8	6	960,0	3,67
VT-03	L4–L5	2	952,5	3,64
VT-04	L8–L9	2	922,5	3,53

INSERTOS POR VIGA — mm


MARCA	DESCRIÇÃO	QT	POSIÇÃO
TB-1	Tubo Ø50×3,0 L=280 a prumo (no dente)	2	a 10 cm das pontas
CH-A3	Chapa 200×150×9,5 + 2 grapas Ø10	2	fundo das pontas
AL-1	Laço de cordoalha Ø12,7	2	a L/5 das pontas

LEGENDA DAS ARMADURAS

- longitudinal (barras N, tirantes, pele)
- transversal (estribos, grampos, suspensão, costura)


NOTAS

1. Todas no mesmo nível: fundo +7,50, topo +8,10, atrás da fiada de placas +7,50/+8,75 (placa inteira por fora); dentes Gerber 30 × 20 nos consolos CP-VT dos pilares (assento +7,79).
2. Linha 4 sem verga: os portões ficam sob a TS-01 da linha 4, livres até +7,50.
3. Linhas 2-4 (vistas E e F) abertas até +7,50: a VT fica aparente por dentro e escondida por fora pela fiada +7,50.
4. Cotas de concreto em cm, níveis em m. Não medir no desenho. PROJETO DA ND ENGENHARIA — PARA APROVAÇÃO, NÃO EXECUTAR.

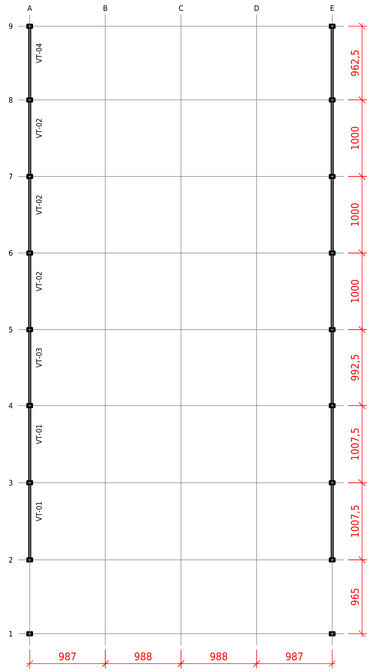


PLANTA — VT (+7,50 / +8,10)

ESC. 1:400 — COTAS EM CM — eixos A e E, linhas 2 a 9

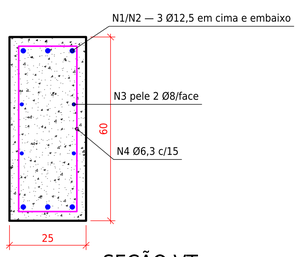

SEÇÃO VT

ESC. 1:10 — COTAS EM CM — 25 × 60, C40

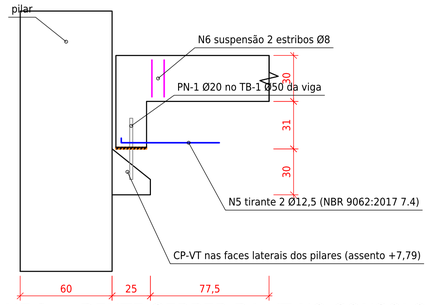

DETALHE 1 — DENTE GERBER DA VT NO CONSOLO CP-VT

ESC. 1:20 — COTAS EM CM — dente 30 × 20; CP-VT + PN-1 Ø20; neoprene 200×150×10

1º DIEDRO

REV	DATA	DESCRIÇÃO
02	12/10/2026	GEOMETRIA DO R01; VT A +7,50/+8,10 ATRÁS DA FIADA +7,50; SEM VERGAS (P
01	12/10/2026	VT/VV A +6,25/+6,85 COM DENTES GERBER

ND — ND ENGENHARIA E ASSESSORIA LTDA — PARA APROVAÇÃO

CNPJ 46.745.157/0001-47 · ndengenharia.com · WhatsApp (46) 92000-4685 · Saudade do Iguaçu/PR

RESP. TÉCNICO: Eng. Civil Nathan Henrique Delgado — CREA-SC 168298-1

ART Nº: _____

CLIENTE: MARQUES ENGENHARIA E CONSTRUÇÕES

OBRA: LETSARA — PAVILHÃO COM MEZANINO

LOCAL: A CONFIRMAR

CONTEÚDO: VIGAS DE TRAVAMENTO VT 25 × 60 (EIXOS A E E, +7,50 A +8,10, DENTES GERBER) — PLANTA, ELEVAÇÃO, SEÇÃO E APOIO

ESCALA	DATA	DESENHO	VERIFICADO	APROVADO
INDICADAS	12/10/2026	ND Engenharia	-	-

DESENHO Nº	REV.	FOLHA	FORMATO
ND-LET-VT01	02	01/01	A1