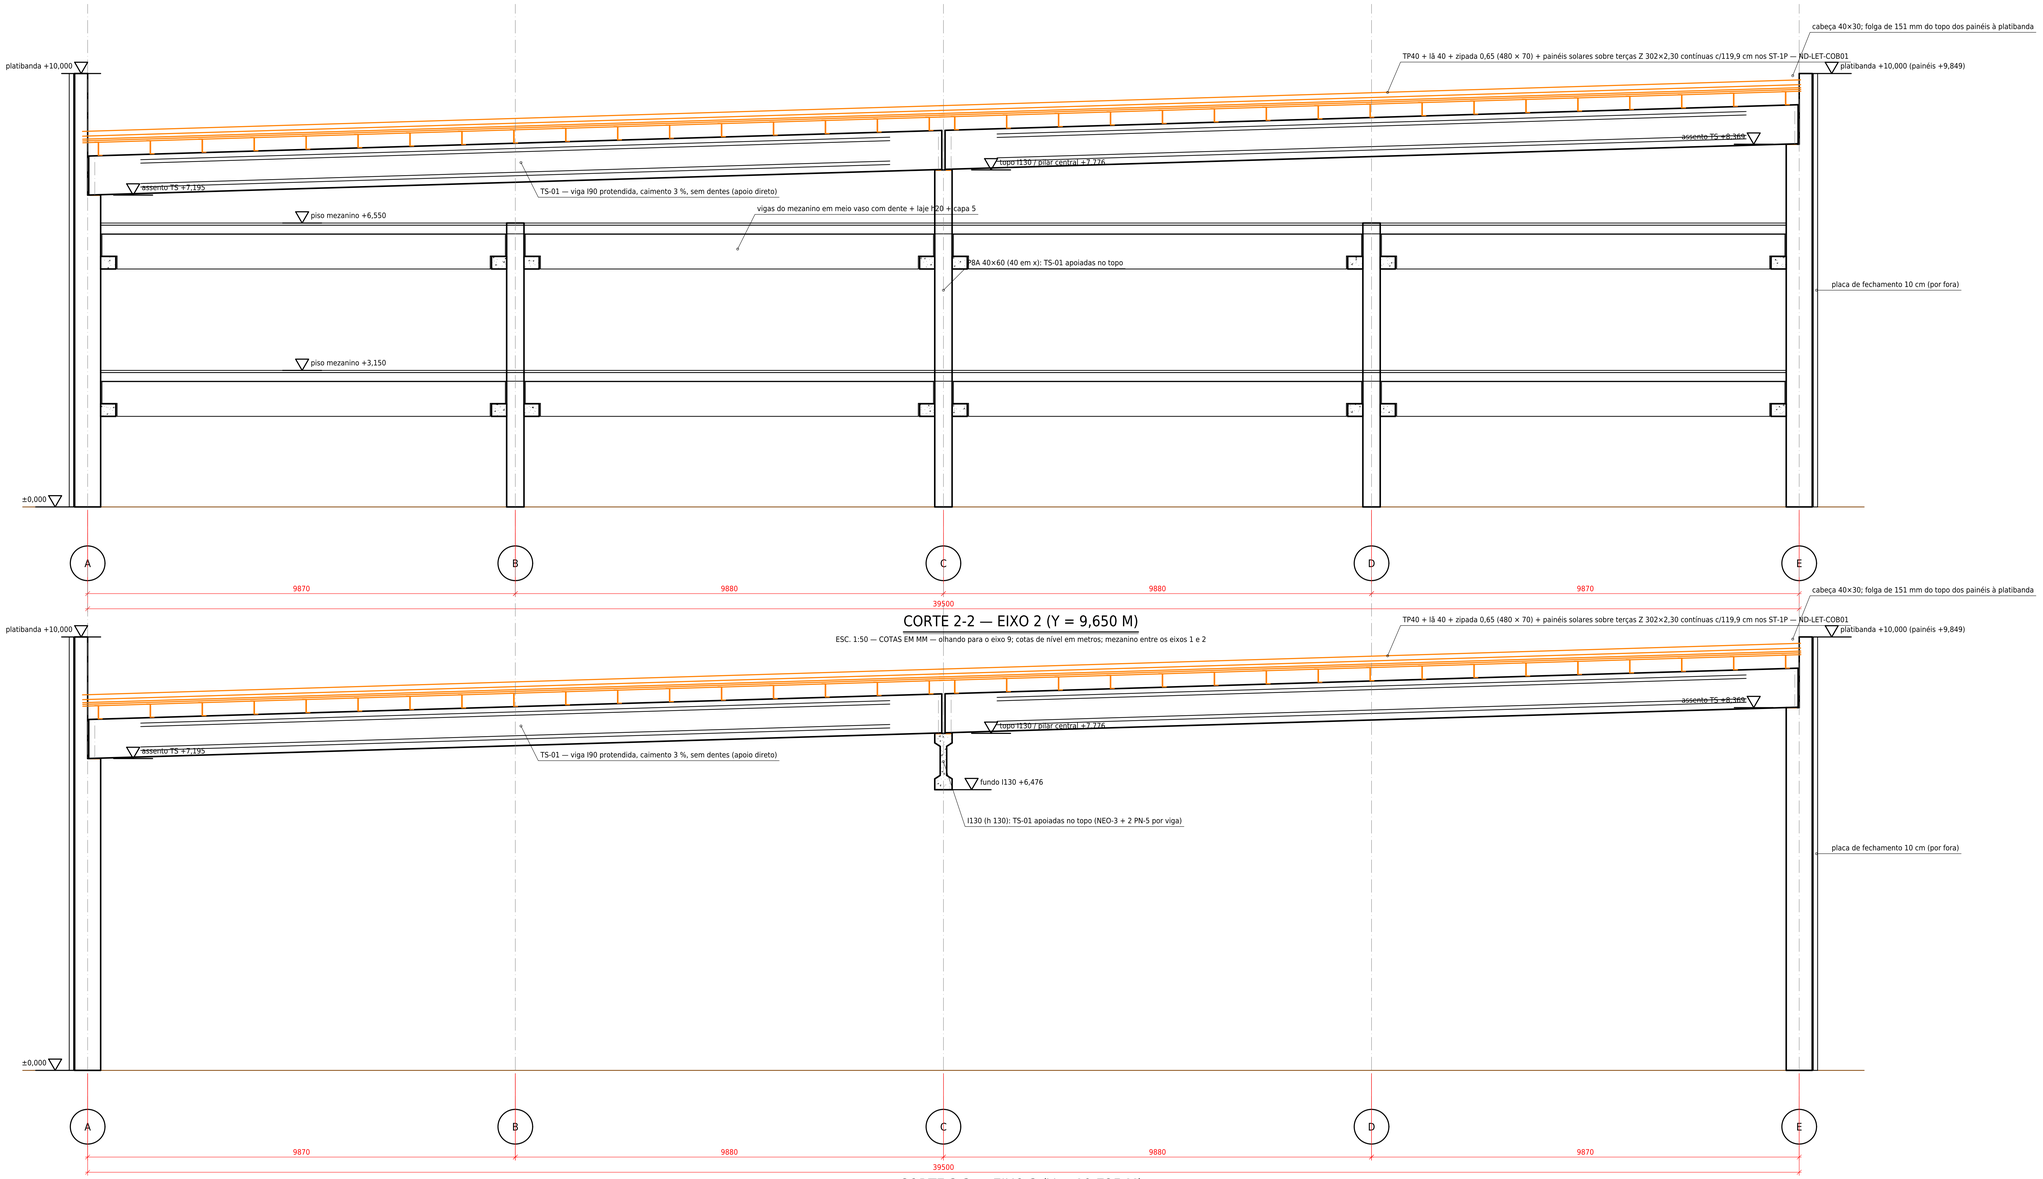


CORTE 2-2 — EIXO 2 (Y = 9,650 M)

ESC. 1:50 — COTAS EM MM — olhando para o eixo 9; cotas de nível em metros; mezanino entre os eixos 1 e 2

CORTE 3-3 — EIXO 3 (Y = 19,725 M)

ESC. 1:50 — COTAS EM MM — olhando para o eixo 9; cotas de nível em metros

NÍVEIS (m)

ELEMENTO	NÍVEL
Assento da TS-01 no P1 (recuo)	+7,195
Assento da TS-01 no P2 (recuo)	+8,369
Topo da I130 / pilares centrais	+7,776
Fundo da I130	+6,476
Assento da I130 (CP-I130)	+6,966
Topo dos painéis junto ao P1 / ao P2	+8,665 / +9,849
Platibanda (todas)	+10,000
Pisos do mezanino	+3,150 / +6,550

NOTAS

1. Cortes gerados do mesmo modelo usado na checagem das ligações.
2. Cobertura rebaixada (rev03) para o pacote TP40 + lã 40 + zipada 70 + painéis solares: topo dos painéis junto ao P2 em +9,849, 151 mm abaixo da platibanda +10,000 (pedido: ≥ 150 mm).
3. TS-01 com 19,696 m entre pontas (a prumo), sem dentes: apoio de 27,5 cm no recuo dos pilares laterais (NEO-4 + 2 PN-3 Ø25) e de 16,25 cm no topo da I130 / pilar central (NEO-3 + 2 PN-5 Ø20); terças c/1,199 m.
4. Cabeça dos pilares laterais recuada acima do assento da TS-01: só os 30 cm externos sobem até +10,00 (consolos externos pela cabeça).
5. Vigas centrais I130 (h 130) com dentes 78 × 35 nos consolos CP-I130; vigas do mezanino VM em meio vaso com dente Gerber nos consolos CP-MEZ (fundo alinhado; rev04, ND-LET-VM01).
6. Pé-direito (rev03): fundo da TS-01 de +7,19 (eixo A) a +7,78 (eixo C); no mezanino superior (+6,55), fundo das terças entre as linhas 1 e 2 de +8,105 (eixo A) a +7,786 (eixo C) — conferir o uso do piso superior. Portões da linha 4 livres até +7,40.
7. Fundações e cálices em projeto próprio. PROJETO DA ND ENGENHARIA — PARA APROVAÇÃO, NÃO EXECUTAR.

DETALHE 1 — APOIO NO PILAR P1 — LADO BAIXO

ESC. 1:20 — COTAS EM MM

DETALHE 2 — APOIO NO TOPO DA I130 — EIXO 3

ESC. 1:20 — COTAS EM MM

DETALHE 3 — APOIO NO PILAR P2 — LADO ALTO

ESC. 1:20 — COTAS EM MM

REV	DATA	DESCRIÇÃO
05	17/10/2026	TERÇAS Z 302 CONTÍNUAS POR TRANSPASSE, SEM MÃO-FRANCESA
04	16/10/2026	NBR 9062: SEM VT; MEZANINO EM MEIO VASO COM DENTE
03	14/10/2026	TS-01 SEM DENTES (APOIO NO RECUO E NO TOPO DA I130); PACOTE COM PAINÉI
02	17/10/2026	CONSOLOS SEM CHANFRO (FUNDO ALINHADO À VIGA); VM I90 COM DENTE 45×30;
01	17/10/2026	geometria do R01 (79,35 × 39,50 m); cabeça dos pilares laterais recuad

ND — ND ENGENHARIA E ASSESSORIA LTDA — PARA APROVAÇÃO

CNPJ 46.741.157/0001-47 · ndengenharia.com · WhatsApp (46) 92000-4685 · Saudade do Iguaçu/PR

RESP. TÉCNICO: Eng. Civil Nathan Henrique Delgado — CREA-SC 168298-1

ART Nº: _____

CLIENTE: MARQUES ENGENHARIA E CONSTRUÇÕES

OBRA: LETSARA — PAVILHÃO COM MEZANINO

LOCAL: A CONFIRMAR

CONTEÚDO: CORTES TRANSVERSAIS DA ESTRUTURA (EIXOS 2 E 3) E APOIOS DA COBERTURA

ESCALA	DATA	DESENHO	VERIFICADO	APROVADO
INDICADAS	17/10/2026	ND Engenharia	-	-

DESENHO Nº	REV.	FOLHA	FORMATO
ND-LET-CT01	05	01/01	A0

1º DIEDRO