
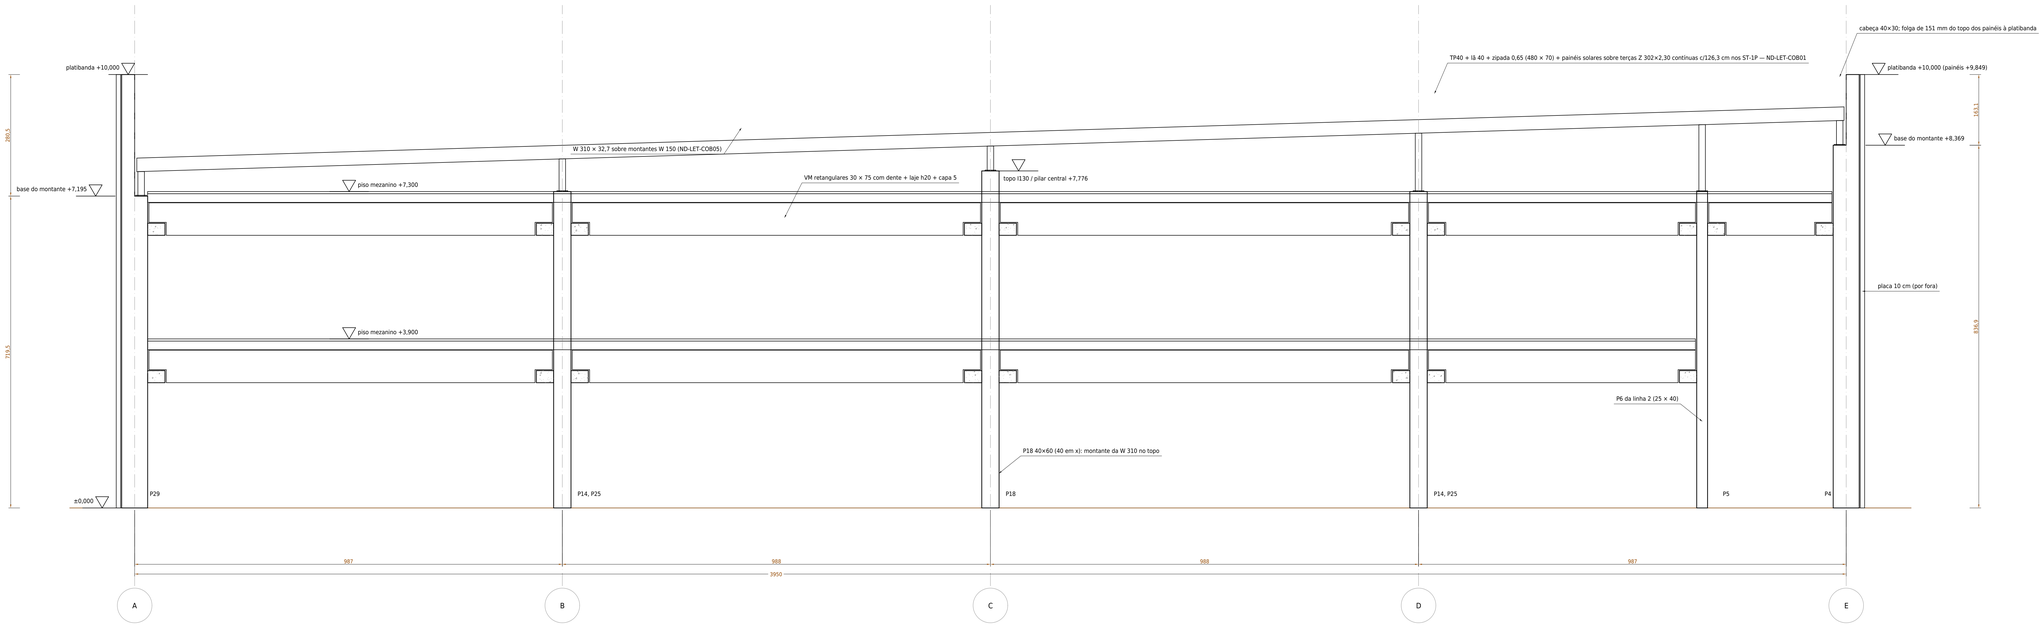


CORTE 2-2 — EIXO 2 (Y = 9,650 M)

ESC. 1:50 — COTAS EM CM — olhando para o eixo 9; níveis em metros; mezanino entre os eixos 1 e 2

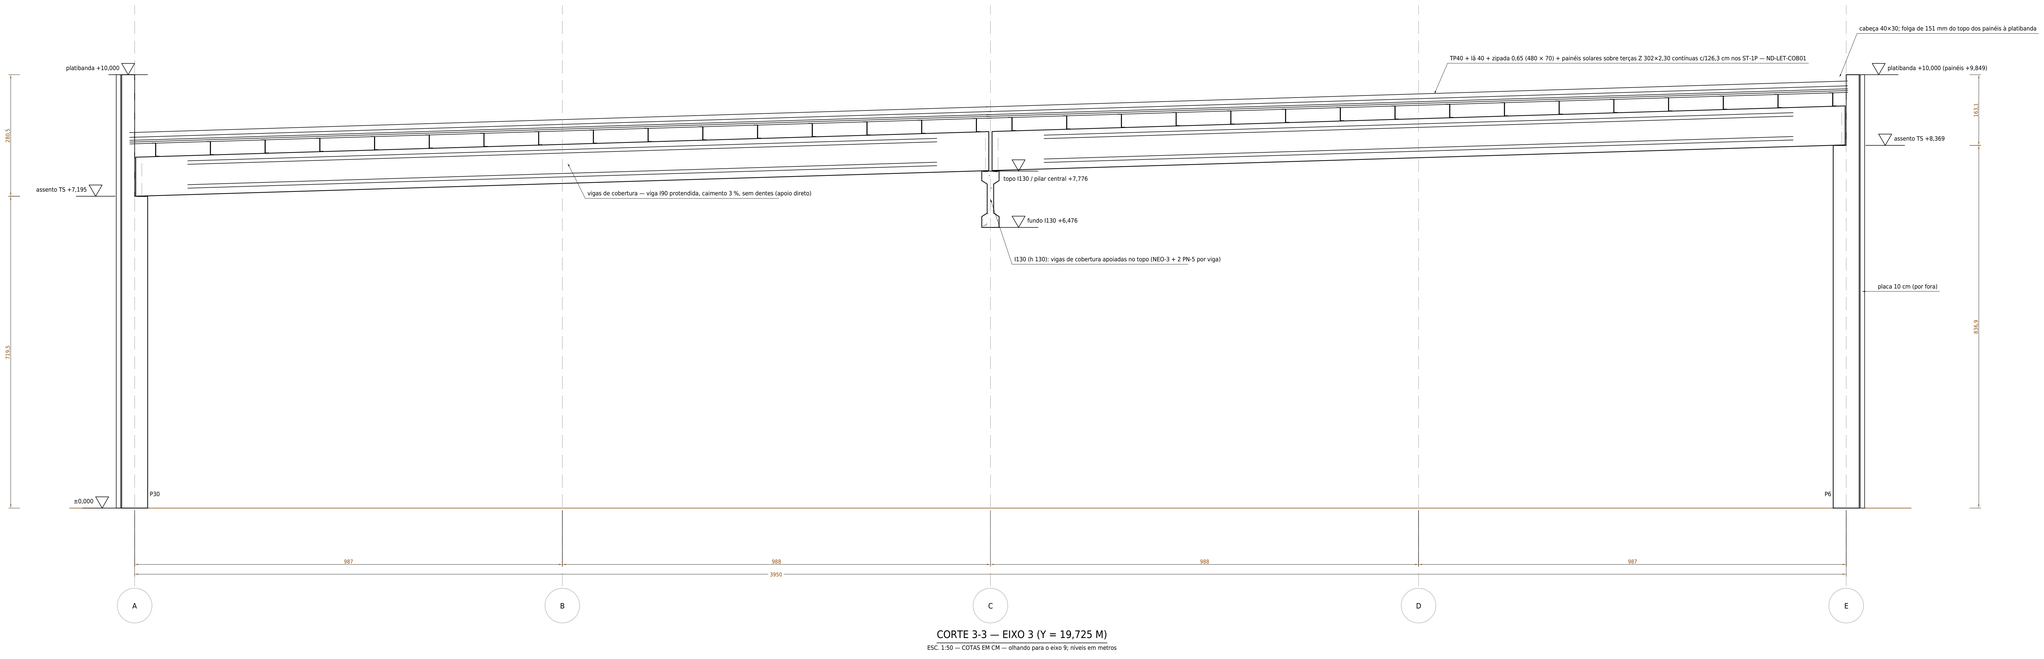

CORTE 3-3 — EIXO 3 (Y = 19,725 M)

ESC. 1:50 — COTAS EM CM — olhando para o eixo 9; níveis em metros

NÍVEIS (m)

ELEMENTO	NÍVEL
Assento da viga de cobertura nos pilares do eixo A (recuo)	+7,195
Assento da viga de cobertura nos pilares do eixo E (recuo)	+8,369
Topo da I130 / pilares centrais	+7,776
Fundo da I130	+6,476
Assento da I130 (CP-I130)	+6,966
Topo dos painéis junto aos pilares do eixo A / aos pilares do eixo E	+8,665 / +9,849
Platibanda (todas)	+10,000
Pisos do mezanino	+3,900 / +7,300

NOTAS

1. Cortes gerados do mesmo modelo usado na checagem das ligações.
2. Cobertura rebaixada (rev03) para o pacote TP40 + lâ 40 + zipada 70 + painéis solares: topo dos painéis junto aos pilares do eixo E em +9,849; 151 mm abaixo da platibanda +10,000 (pedido: ≥ 150 mm).
3. vigas de cobertura com 19,696 m entre pontas (a prumo), sem dentes: apoio de 27,5 cm no recuo dos pilares laterais (NEO-4 + 2 PN-3 Ø25) e de 16,25 cm no topo da I130 / pilar central (NEO-3 + 2 PN-5 Ø20); terças c/1,263 m.
4. Cabeça dos pilares laterais recuada acima do assento da viga de cobertura: só os 30 cm externos sobem até +10,00 (consolos externos pela cabeça).
5. Vigas centrais I130 (h 130) com dentes 78 × 35 nos consolos CP-I130; vigas do mezanino VM retangulares 30 × 75 protendidas com dente Gerber nos consolos CP-MEZ (fundo alinhado; rev09; ND-LET-VM01). Eixo 2: sem vigas de cobertura — W 310 × 32,7 metálica contínua sobre montantes W 150 nos pilares (DEC-049).
6. Pé-direito (rev03): fundo da viga de cobertura de +7,19 (eixo A) a +7,78 (eixo C); na laje superior (+7,30, sem uso), fundo das terças entre as linhas 1 e 2 de +8,105 (eixo A) a +7,786 (eixo C) — conferir o uso do piso superior. Portões da linha 4 livres até +7,40.
7. Detalhes de cada apoio na montagem: ND-LET-CT04. Corte do mezanino: ND-LET-CT02. Corte longitudinal: ND-LET-CT03.
8. Cotas em cm, níveis em m. Fundações e cálices em projeto próprio. EMISSÃO EXECUTIVA — LIBERADO PARA PRODUÇÃO, ARMAÇÃO, CONCRETAGEM E MONTAGEM.

REV	DATA	DESCRIÇÃO
09	23/10/2026	DEC-045/047/048/049: PISOS +3,90/+7,30; VM 30 × 75; EIXO 2 COM W 310 M
08	21/10/2026	EMISSÃO EXECUTIVA — LIBERADO PARA PRODUÇÃO E MONTAGEM
07	21/10/2026	COTAS EM CM; MARCAS DOS PILARES NOS CORTES; DETALHES DE APOIO PASSAM P
05	17/10/2026	TERÇAS Z 302 CONTÍNUAS POR TRANSPASSE, SEM MÃO-FRANCESA
04	16/10/2026	NBR 9062: SEM VT; MEZANINO EM MEIO VÃO COM DENTE
03	14/10/2026	TS-01 SEM DENTES (APOIO NO RECUO E NO TOPO DA I130); PACOTE COM PAINÉI
02	12/10/2026	CONSOLOS SEM CHANFRO (FUNDO ALINHADO À VIGA); VM 080 COM DENTE 45×30;
01	12/10/2026	geometria do R01 (78,35 × 39,50 m); cabeça dos pilares laterais recuad

ND ENGENHARIA E ASSESSORIA LTDA
CNPJ 46.743.157/0001-47 · ndengenharia.com · WhatsApp (46) 9)000-4685 · Saudade do Iguaçu/PR
RESP. TÉCNICO: Eng. Civil Nathan Henrique Delgado — CREA-SC 168298-1
ART Nº _____

EXECUTIVO — LIBERADO

CLIENTE: MARQUES ENGENHARIA E CONSTRUÇÕES
OBRA: LETSARA — PAVILHÃO COM MEZANINO
LOCAL: A CONFIRMAR

CONTEÚDO: CORTES TRANSVERSAIS DA ESTRUTURA — EIXOS 2 E 3

ESCALA	DATA	DESENHO	VERIFICADO	APROVADO
1:50	23/10/2026	ND Engenharia	-	-

DESENHO Nº	REV.	FOLHA	FORMATO
ND-LET-CT01	09	01/01	A0

3º DIEDRO