
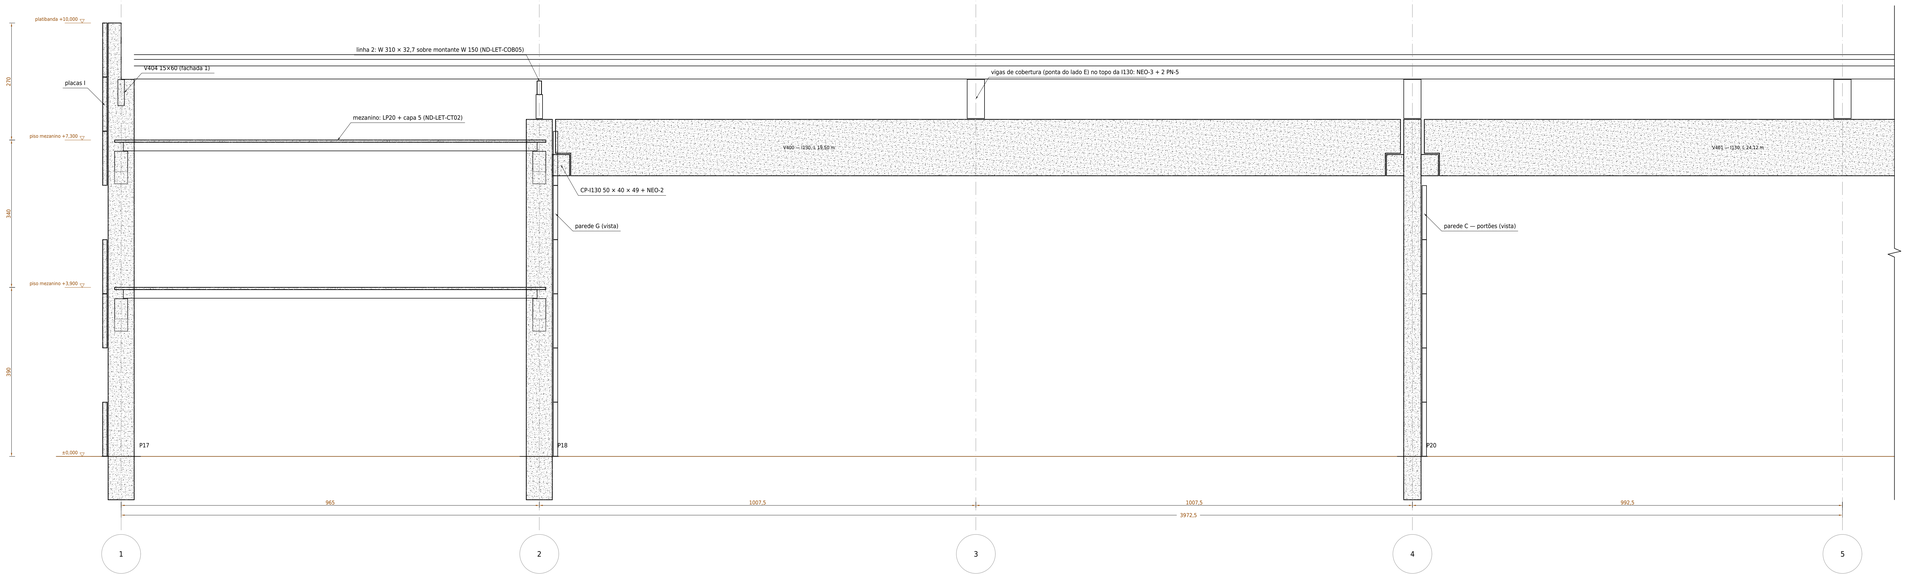


CORTE 6-6 — LONGITUDINAL NO EIXO C (X = 19,75 M) — LINHAS 1 A 5

ESC. 1:50 — COTAS EM CM — olhando para o eixo E; pilares do eixo C e vigas I130 cortados; vigas de cobertura do lado E no topo da I130; mezanino entre as linhas 1 e 2; continua abaixo

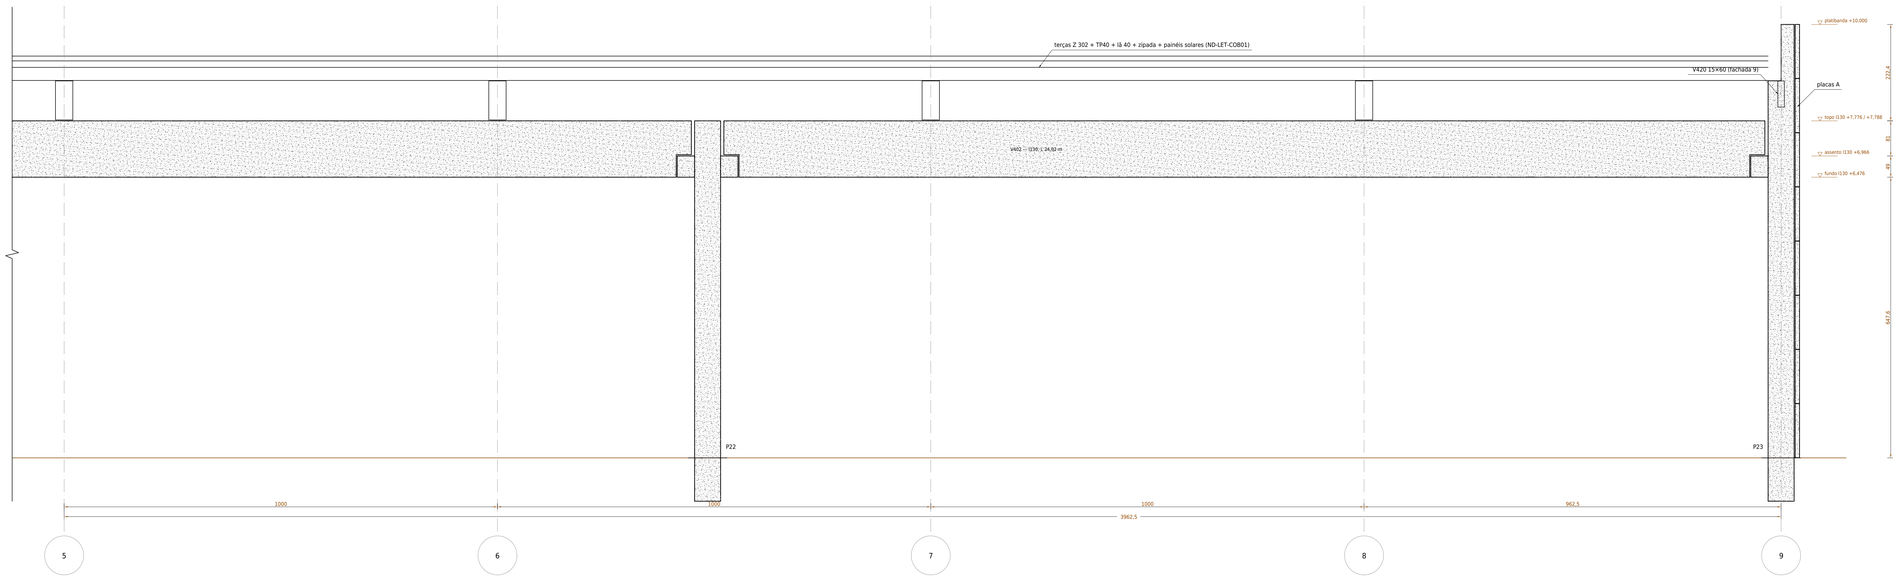

CORTE 6-6 (CONTINUAÇÃO) — LINHAS 5 A 9


ESC. 1:50 — COTAS EM CM — olhando para o eixo E; continuação do corte acima a partir da linha 5

CORTES DA OBRA

CORTE	POSIÇÃO	FOLHA
1-1	pórtico de montagem, linha 3	ND-LET-MON01
2-2	transversal, eixo 2	ND-LET-CT01
3-3	transversal, eixo 3	ND-LET-CT01
4-4	mezanino, meio do vão das lajes	ND-LET-CT02
5-5	mezanino, entre os eixos B e C	ND-LET-CT02
6-6	longitudinal, eixo C	ND-LET-CT03
M-M	montagem do mezanino	ND-LET-MON02


NOTAS

1. Corte 6-6 gerado da mesma geometria do modelo e das pranchas das peças: pilares do eixo C cortados (P17 e P23 com a cabeça recuada no lado interno acima de +8,70); vigas centrais I130 cortadas no eixo, consolos CP-I130 no plano.
2. I130: V400 (P18 → P20), V401 (P20 → P22), V402 (P22 → P23); folga de 7,5 cm entre o nariz do dente e a face do pilar; assento +6,966 com NEO-2 300 × 200 × 31 fretado e PN-2 Ø25 grauteado numa ponta só.
3. V407, V408 das linhas 3 a 8 apoiadas no topo da I130 (lado A +7,776, lado E +7,788) com NEO-3 e 2 PN-5 por viga; folga de 7,5 cm entre as pontas no eixo C (ND-LET-CT04, det. 2). Na linha 2 a cobertura é a W 310 × 32,7 metálica contínua sobre montantes W 150 nos pilares (DEC-048, ND-LET-COB05).
4. Placas de fechamento por fora dos pilares nas fachadas I (linha 1) e A (linha 9); paredes internas G (linha 2) e C (linha 4, portões) do lado do pavilhão; cada placa nos seus 2 consolos, folgas de 0,5 cm na altura e 2 cm no comprimento.
5. Cortes transversais: ND-LET-CT01 (eixos 2 e 3); mezanino: CT02; apoios como montados: CT04; montagem: MON01 a MON03.
6. Cotas em cm, níveis em m. Não medir no desenho. EMISSÃO EXECUTIVA — LIBERADO PARA PRODUÇÃO, ARMAÇÃO, CONCRETAGEM E MONTAGEM.

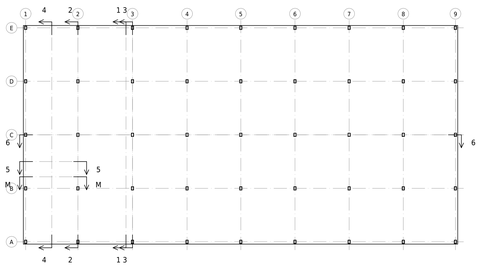

PLANTA-CHAVE DOS CORTES

ESC. 1:400 — COTAS EM CM — posição de cada corte do jogo executivo e a folha onde está

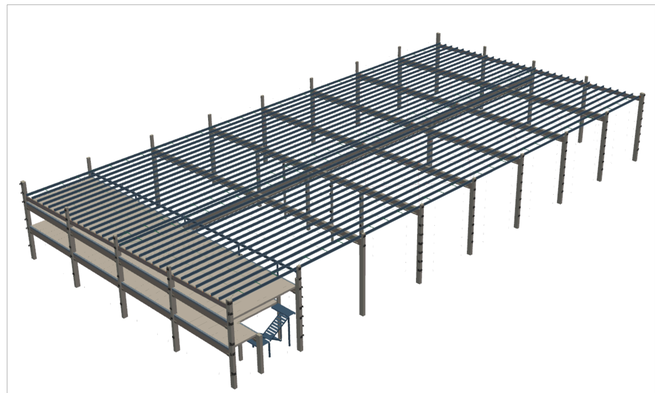

3D — ESTRUTURA COMPLETA

modelo da obra sem telhas e placas



3D — RECORTE NO EIXO C

pilares centrais, I130 e vigas de cobertura apoiadas no topo

REV	DATA	DESCRIÇÃO
02	23/10/2026	DEC-045/047/048/049: PISOS +3,90/+7,30; VM 30 × 75; LINHA 2 METÁLICA I
01	21/10/2026	EMISSÃO EXECUTIVA — LIBERADO PARA PRODUÇÃO E MONTAGEM
00	21/10/2026	EMISSÃO: CORTE 6-6 LONGITUDINAL, PLANTA-CHAVE DOS CORTES E 3D

ND ENGENHARIA E ASSESSORIA LTDA
CNPJ 46.745.157/0001-47 · ndengenharia.com · WhatsApp (46) 92000-4685 · Saudade do Iguaçu/PR
RESP. TÉCNICO: Eng. Civil Nathan Henrique Delgado — CREA-SC 168298-1
ART Nº _____

EXECUTIVO — LIBERADO

CLIENTE: MARQUES ENGENHARIA E CONSTRUÇÕES
OBRA: LETSARA — PAVILHÃO COM MEZANINO
LOCAL: A CONFIRMAR

CONTEÚDO: CORTE LONGITUDINAL DA OBRA (EIXO C), PLANTA-CHAVE DOS CORTES E VISTAS 3D DA ESTRUTURA

ESCALA	DATA	DESENHO	VERIFICADO	APROVADO
INDICADAS	23/10/2026	ND Engenharia	-	-

DESENHO Nº	REV.	FOLHA	FORMATO
ND-LET-CT03	02	01/01	A0

1º DIEDRO