


PLANTA DE LOCAÇÃO DOS PILARES

ESC. 1:100 — COTAS EM CM — eixos do R01 (Marques); pilares centrados nos eixos, exceto onde cotado

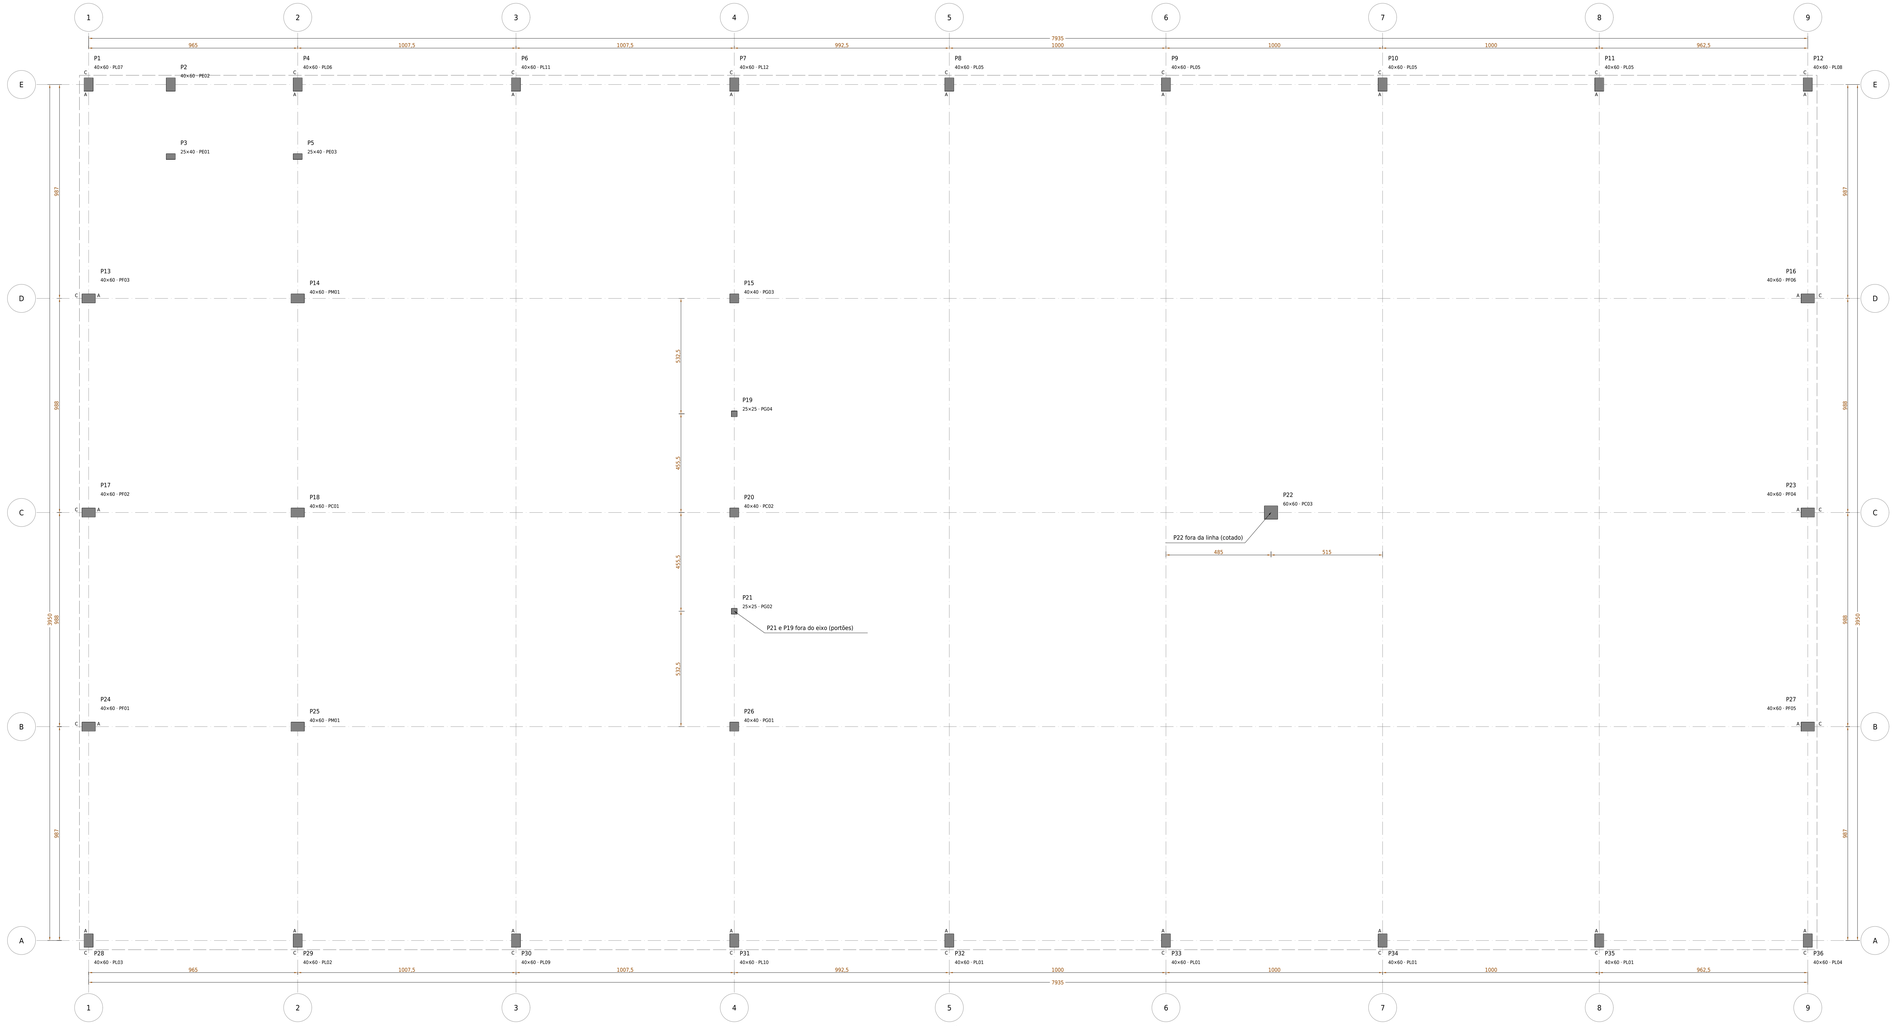


DETALHE 1 — PILAR LATERAL

ESC. 1:25 — COTAS EM CM — PL: 40×60, 60 na direção A-E

DETALHE 2 — PILAR DE FACHADA

ESC. 1:25 — COTAS EM CM — PF: 40×60, 60 na direção 1-9

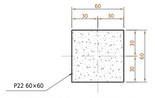

DETALHE 3 — CENTRAIS

ESC. 1:25 — COTAS EM CM — P22 60×60 (P18/P14, P25 40×60, P20 40×40)



DETALHE 4 — PORTÕES

ESC. 1:25 — COTAS EM CM — P26/03 40×40; P21/04 25×25

QUADRO DE PILARES — NOME × FOLHA × PROJETO DO CLIENTE (R01)				
PILARES	SEÇÃO (cm)	QT	FOLHA	NOME NO R01
P1	40×60	1	PL07	P2 L1
P2	40×60	1	PE02	P7 (escada)
P3	25×40	1	PE01	P6 (escada)
P4	40×60	1	PL06	P2 L2
P5	25×40	1	PE03	P6 (linha 2)
P6	40×60	1	PL11	P2 L3
P7	40×60	1	PL12	P2 L4
P8, P9, P10, P11	40×60	4	PL05	P2 L5, P2 L6, P2 L7, P2 L8
P12	40×60	1	PL08	P2 L9
P13	40×60	1	PF03	P5 L1
P14, P25	40×60	2	PM01	P8B, P8
P15	40×40	1	PG03	P12
P16	40×60	1	PF06	P5 L9
P17	40×60	1	PF02	P4 L1
P18	40×60	1	PC01	P8A
P19	25×25	1	PG04	P10
P20	40×40	1	PC02	P11
P21	25×25	1	PG02	P10
P22	60×60	1	PC03	P13
P23	40×60	1	PF04	P14 L9
P24	40×60	1	PF01	P3 L1
P26	40×40	1	PG01	P9
P27	40×60	1	PF05	P3 L9
P28	40×60	1	PL03	P1 L1
P29	40×60	1	PL02	P1 L2
P30	40×60	1	PL09	P1 L3
P31	40×60	1	PL10	P1 L4
P32, P33, P34, P35	40×60	4	PL01	P1 L5, P1 L6, P1 L7, P1 L8
P36	40×60	1	PL04	P1 L9
TOTAL		36		inclui P6 e P7 da escada e P6 da linha 2 (DEC-045)

NOTAS

1. Eixos e ordenadas da PLANTA BAIXA — LOCAÇÃO DE PILARES do R01 (Marques Engenharia): 79,35 m entre os eixos 1 e 9 e 39,50 m entre os eixos A e E. Conferir a locação no terreno antes de concretar os blocos.
2. Todos os pilares são centrados nos eixos, exceto P21 e P19 (linha 4, portões) e P22 (entre as linhas 6 e 7): posições cotadas na planta.
3. Faces: A = interna (console da viga principal), C = externa (placas de fechamento, por fora dos pilares, folga 2,5 cm; contorno tracejado). B e D completam no sentido anti-horário visto de cima.
4. Nomes P1 a P33: um por peça, em sentido de leitura desta planta (de cima para baixo, eixo E → A, e da esquerda para a direita, linha 1 → 9). Peças iguais têm a mesma folha de detalhamento (coluna FOLHA). A coluna NOME NO R01 é só correspondência com o projeto do cliente, que usa P1 a P14 com outro significado.
5. Tolerância de locação (NBR 9062:2017 5.2.2.6): ±1,0 cm entre apoios consecutivos, acumulado ≤ 0,1 % do comprimento; prumo ≤H/300 até 2,5 cm.
6. Cargas na fundação: ND-LET-CG01. Cortes: ND-LET-CT01 a CT04 (planta-chave dos cortes na CT03). Montagem: ND-LET-MON01 a MON03.
7. Cotas em cm; níveis em m a partir do piso acabado (±0,00).
8. EMISSÃO EXECUTIVA — LIBERADO PARA PRODUÇÃO, ARMAÇÃO, CONCRETAGEM E MONTAGEM.

REV	DATA	DESCRIÇÃO
09	23/10/2026	DEC-045: P6 E P7 DA ESCADA E P6 DA LINHA 2 (PE-01 A PE-03); NOMES NOVO
08	21/10/2026	EMISSÃO EXECUTIVA — LIBERADO PARA PRODUÇÃO E MONTAGEM
07	21/10/2026	SO LOCAÇÃO DOS PILARES (1:100): EIXOS NOS 4 LADOS, MARCAS, FACES: CORT
06	20/10/2026	X DA COBERTURA NOS VÃOS 4-5 A 8-9; VB-01 A VB-08
05	17/10/2026	TERÇAS Z 302 CONTÍNUAS POR TRANSPASSE
04	16/10/2026	NBR 9062: SEM VT; VB 15×60 COM DENTE
03	14/10/2026	TS-01 SEM DENTES; COBERTURA REBAIXADA: I130; PLACAS 10 cm

ND ENGENHARIA E ASSESSORIA LTDA
CNPJ 46.745.157/0001-47 · ndengenharia.com · WhatsApp (46) 92000-4685 · Saudade do Iguaçu/PR
RESP. TÉCNICO: Eng. Civil Nathan Henrique Delgado — CREA-SC 168298-1
ART Nº: _____

EXECUTIVO — LIBERADO

CLIENTE:	MARQUES ENGENHARIA E CONSTRUÇÕES
OBRA:	LET'S4RA — PAVILHÃO COM MEZANINO
LOCAL:	A CONFIRMAR

CONTEÚDO

PLANTA DE LOCAÇÃO DOS PILARES — EIXOS, MARCAS, SEÇÕES E FACES

ESCALA	DATA	DESENHO	VERIFICADO	APROVADO
INDICADAS	23/10/2026	ND Engenharia	-	-

DESENHO Nº	REV.	FOLHA	FORMATO
ND-LET-LOC01	09	01/01	A0

1º DIEDRO